

DAMT-01-001-SYS-TS8-0-MV-DWG-1100-03

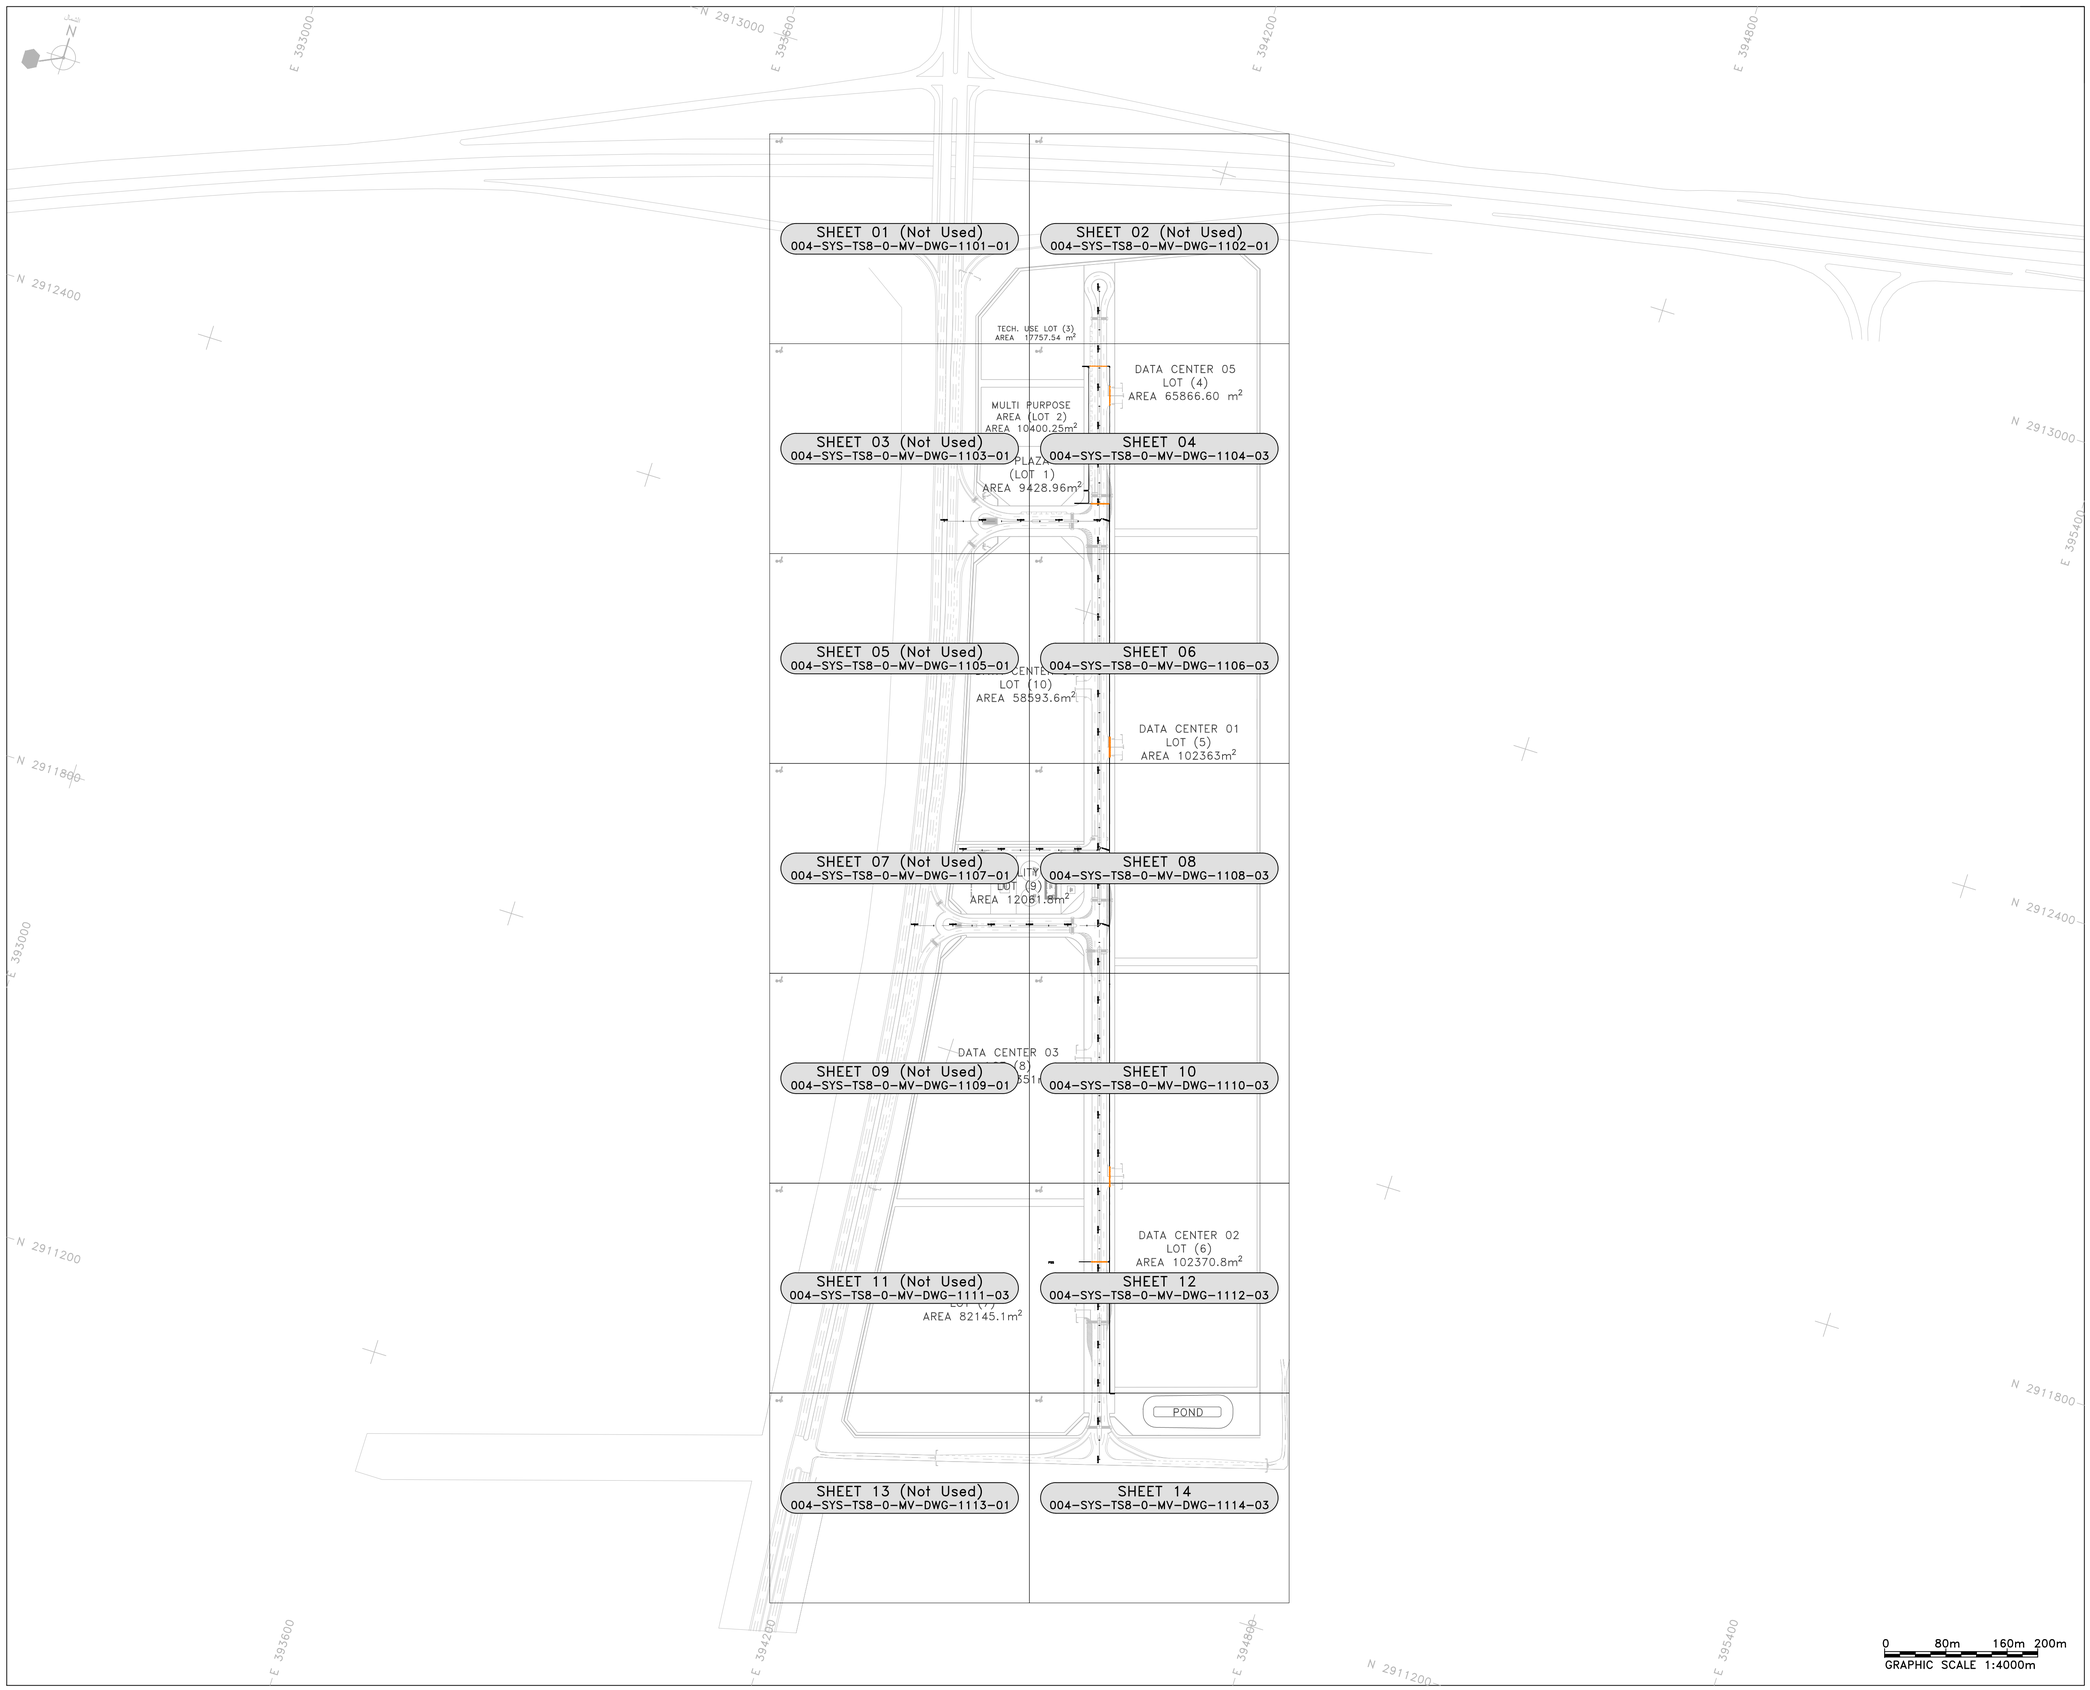

KEY PLAN

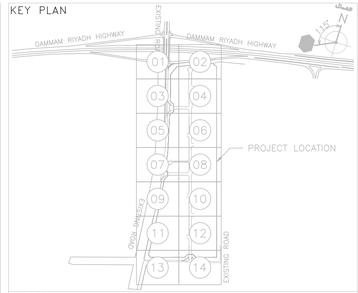

NOTES

1. ALL DIMENSIONS ARE IN MILLIMETERS AND LEVELS ARE IN METERS UNLESS OTHERWISE SPECIFIED.
2. ALL DIMENSIONS ARE TO BE READ AND NOT MEASURED.
3. ANY DISCREPANCIES MUST BE BROUGHT TO THE NOTICE OF THE CONSULTANT BEFORE EXECUTION OF THE WORK AT SITE.
4. ANY DEVIATION FROM APPROVED LAND PLANS TO BE BROUGHT TO THE NOTICE OF THE CONSULTANT BEFORE EXECUTION.
5. THIS DRAWING MUST BE READ IN CONJUNCTION WITH ALL RELEVANT ARCHITECTURE, STRUCTURAL, PLUMBING & FIRE FIGHTING, STREET LIGHTING AND TRAFFIC MANAGEMENT DRAWINGS.
6. LOCATION OF SUBSTATIONS IN LAYOUT ARE INDICATIVE, FINAL LOCATION SHALL BE COORDINATED WITH MODON.
7. MV CABLES FROM PSS TO DATA CENTER 1 TO 5 ARE INDICATIVE ONLY AND SHALL BE DONE DATA CENTER CONTRACTOR.

LEGEND

SYMBOL	DESCRIPTION
SS-XX	UNIT SUBSTATION (RMU, 33KV/400V TRANSFORMER WITH LVDP)
———	1X3Cx400mm²Al. XLPE UNARMORED
	CONCRETE ENCASED DUCT BANK WITH ø150MM UPVC FOR ROAD CROSSING (MV)

REV.	DATE	DESCRIPTION	DRAWN	CHECKED
03	31/08/2025	ISSUED FOR TENDER	AH	LA
02	16/07/2025	ISSUED FOR TENDER	AH	LA
01	09/07/2025	ISSUED FOR TENDER	AH	LA

CLIENT

MODON

DESIGNER

SYSTRA

PROJECT NAME

MASTER PLAN AND INFRASTRUCTURE DESIGN FOR TECHNOLOGY ZONE IN DAMMAM

BUILDING NAME

N/A

DISCIPLINE

ELECTRICAL

DRAWING TITLE

MV CABLE ROUTING LAYOUT PLAN – OVERALL SHEET FOR MODON FACILITIES AND UTILITIES

DRAWING NO.

DAMT-01-001-SYS-TS8-0-MV-DWG-1100-03

SHEET NO.

01 OF 01

DRAWN BY	CHECKED BY	APPROVED BY	REVISION
AH	LA	AA	03
DESCRIPTION		SCALE	DATE
ISSUED FOR TENDER		1:4000	31/08/2025

ORIGINAL DRAWING SIZE:A1

7/2/2025 03:57:53 PM